






Central circulation / connecting block


2nd Floor Plan

Conceptual diagram based on the hand-drawn layouts

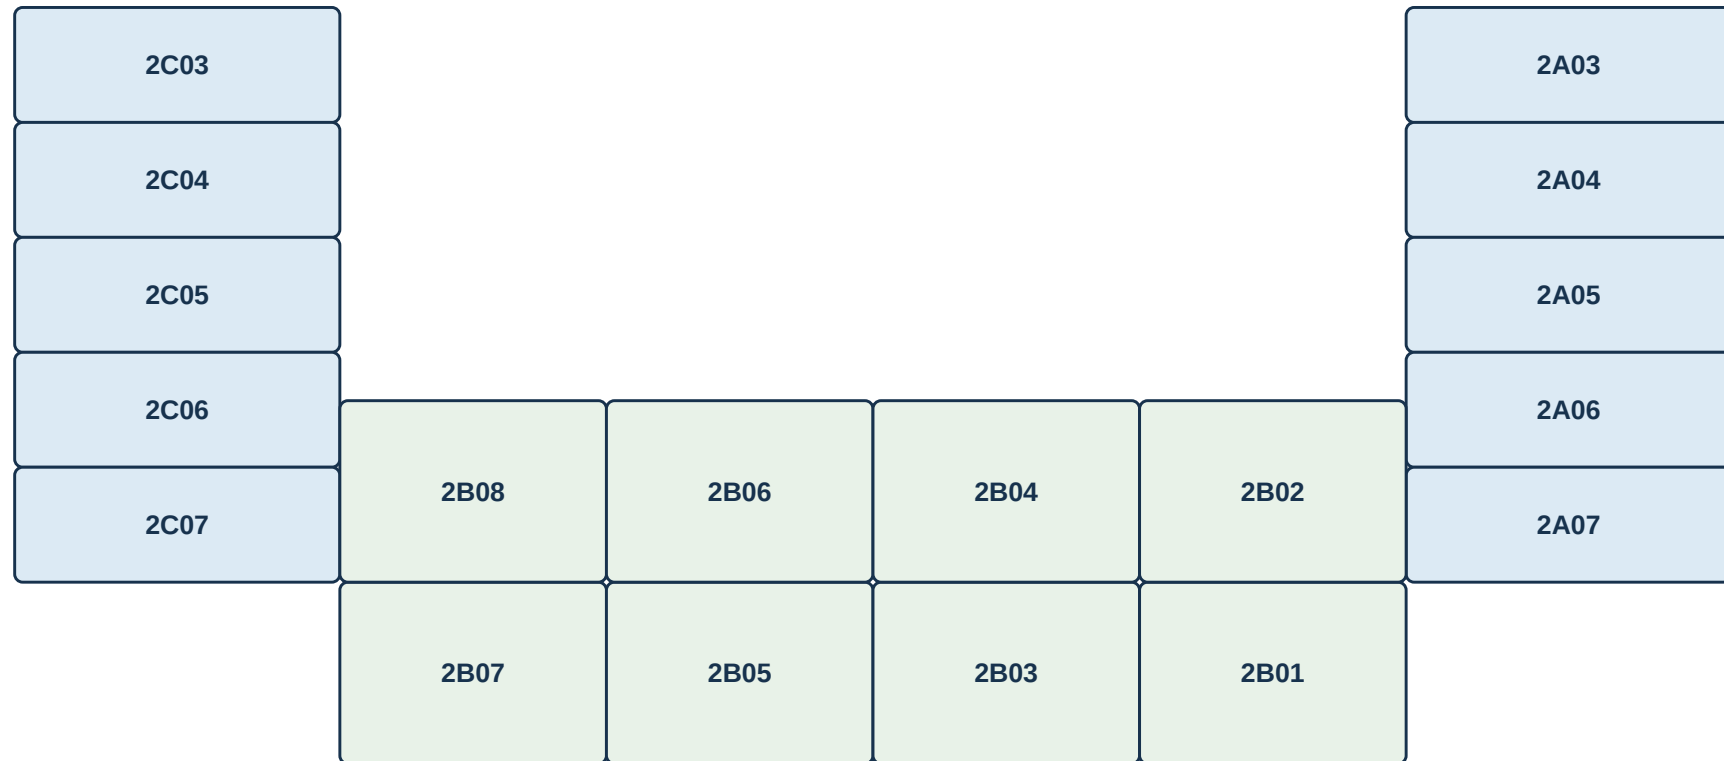


B-block: even rooms on top, odd rooms below

Central circulation / connecting block

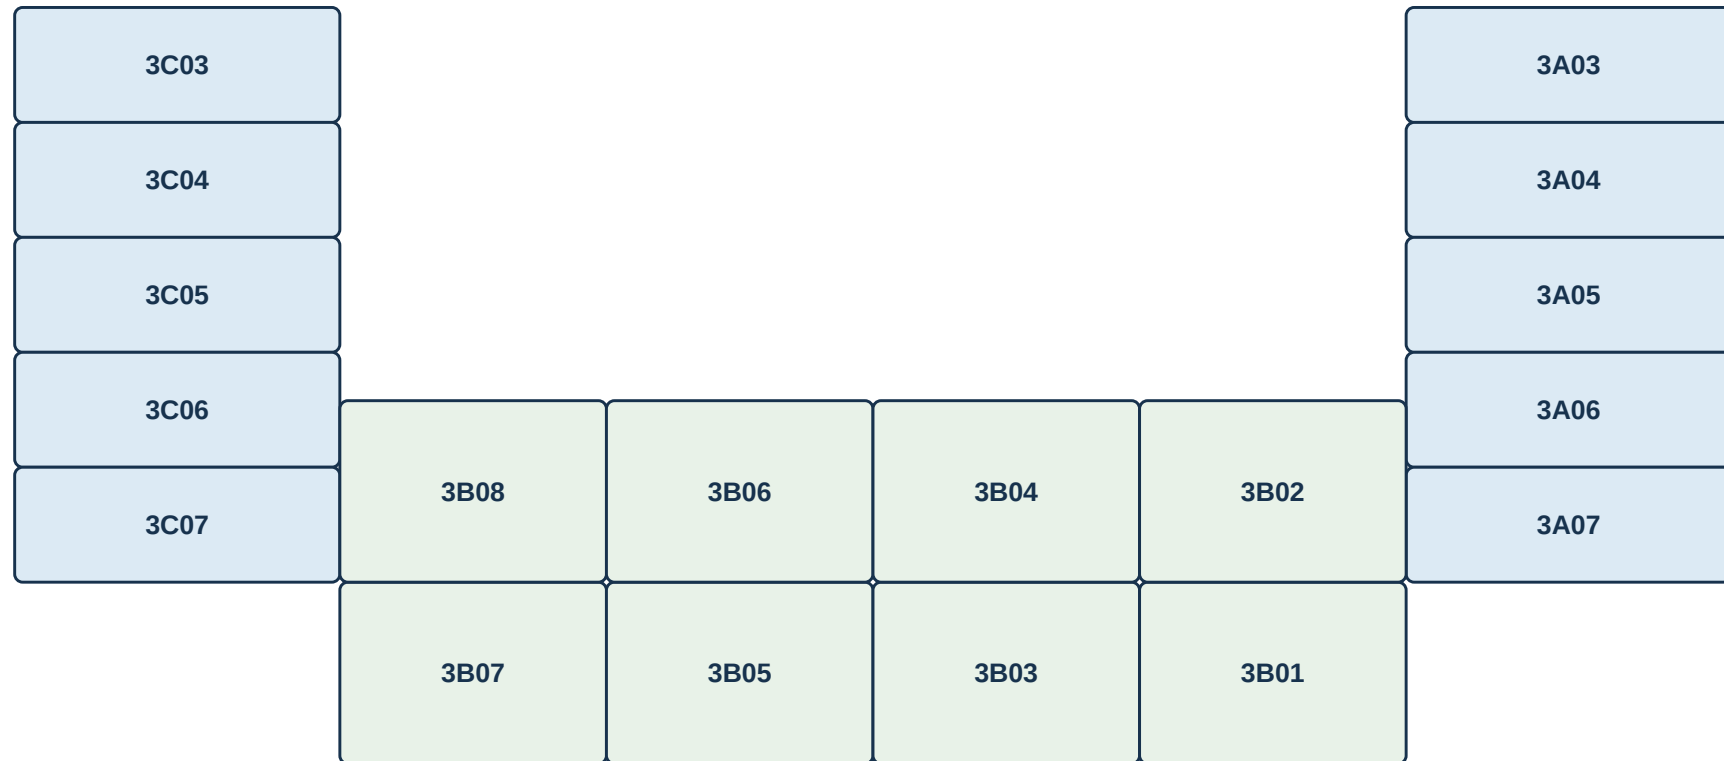


B-block: even rooms on top, odd rooms below

Central circulation / connecting block

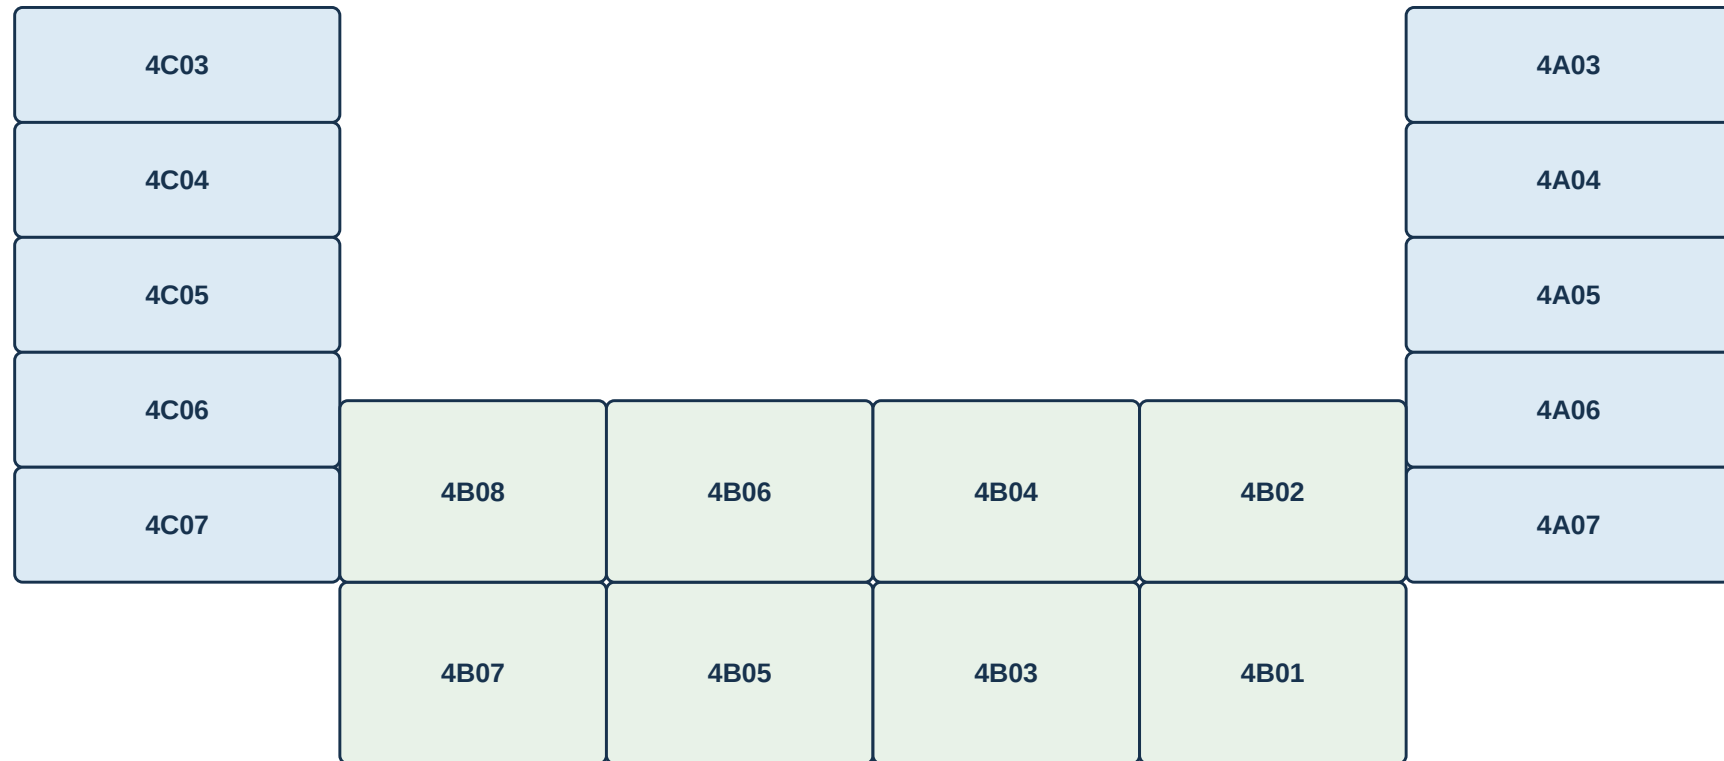


B-block: even rooms on top, odd rooms below

Central circulation / connecting block

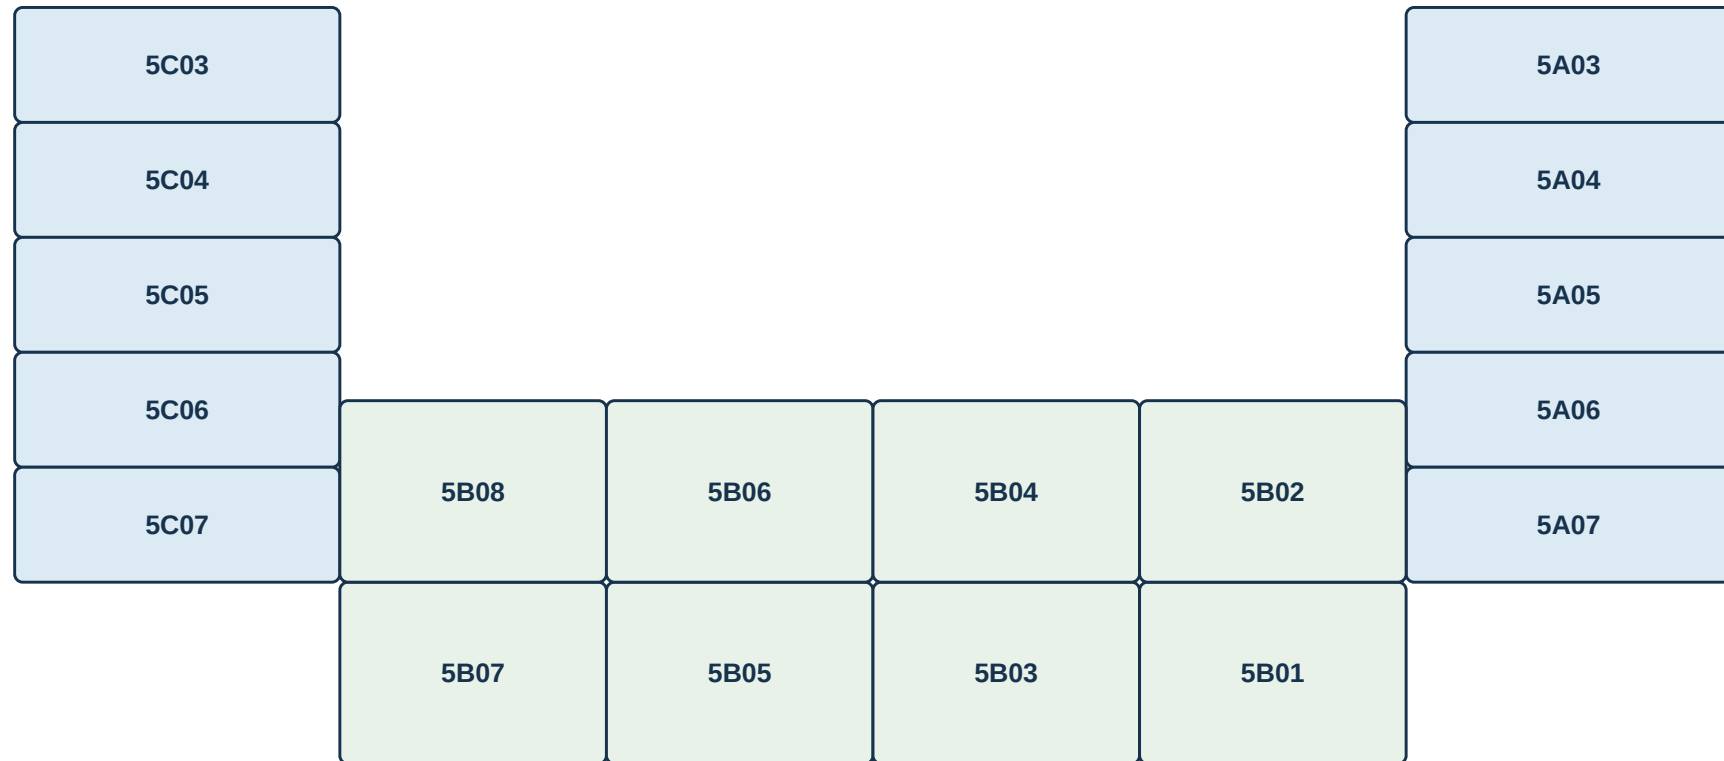


B-block: even rooms on top, odd rooms below

Central circulation / connecting block

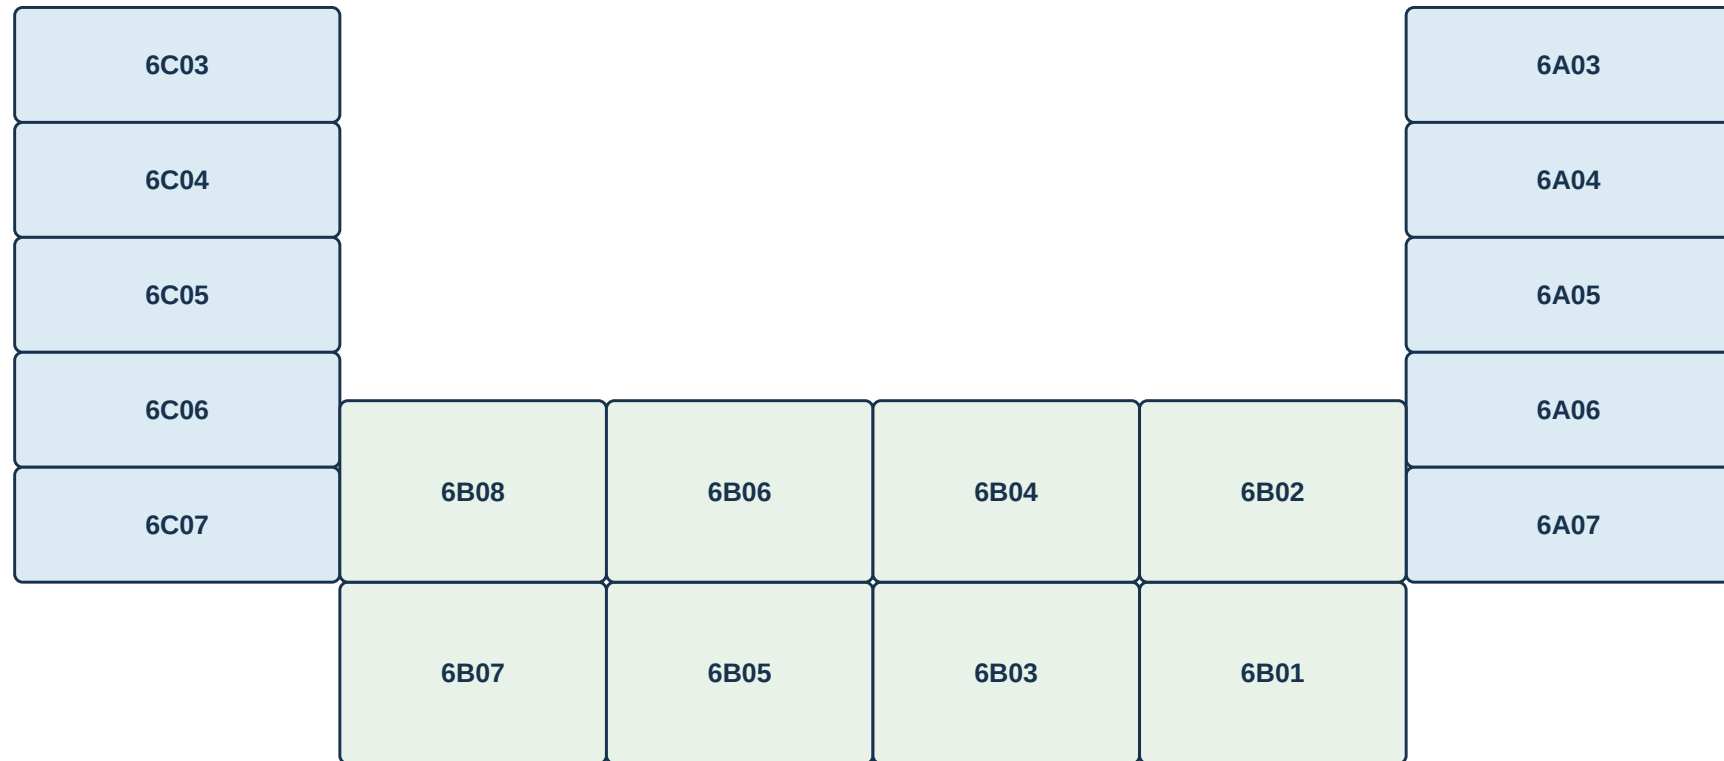


B-block: even rooms on top, odd rooms below

Central circulation / connecting block

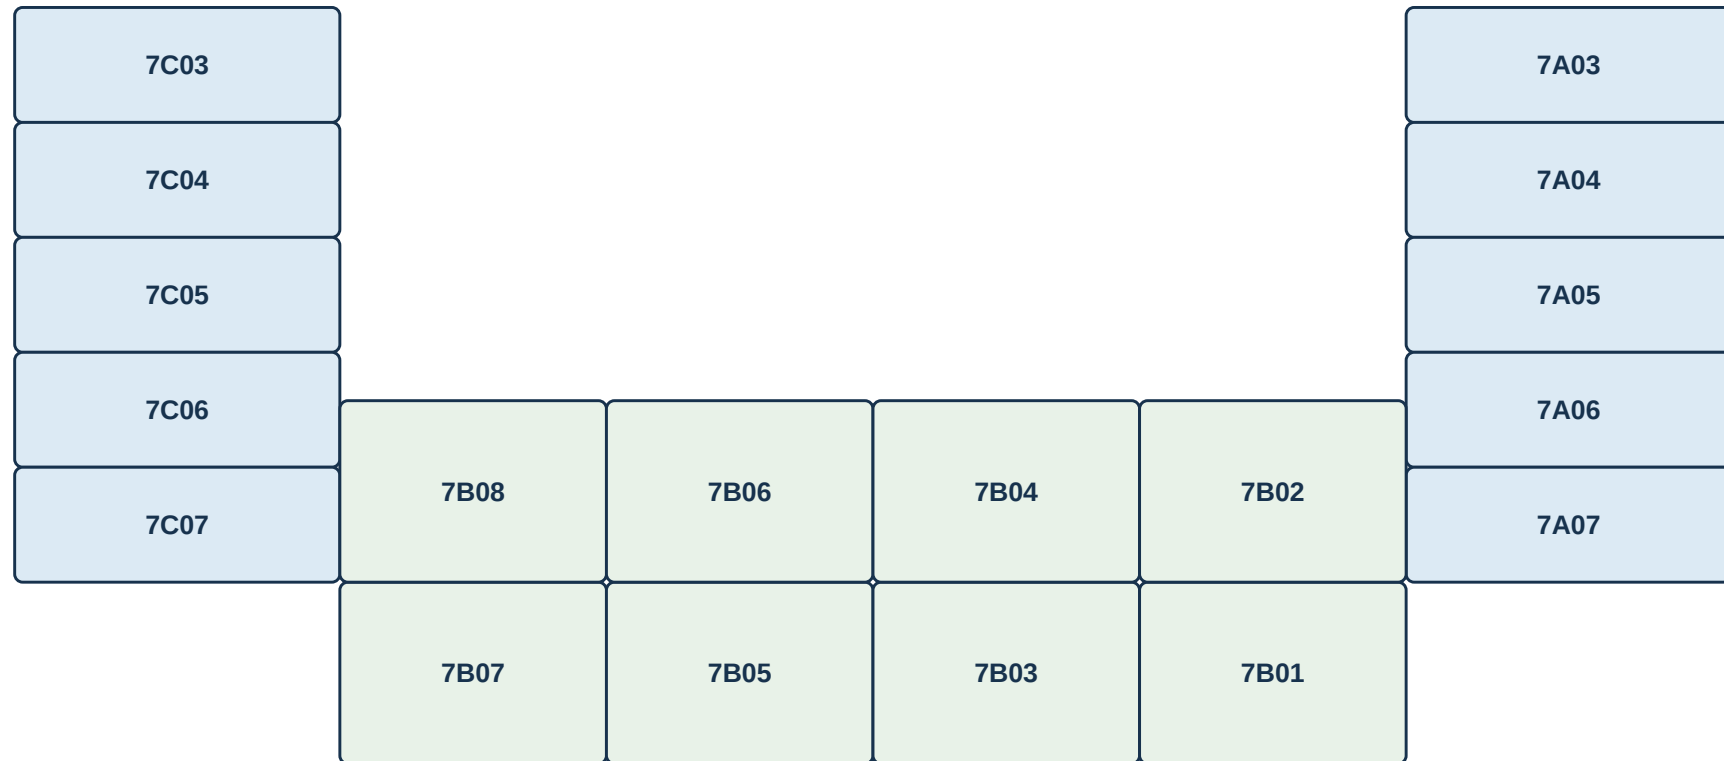


B-block: even rooms on top, odd rooms below

Central circulation / connecting block

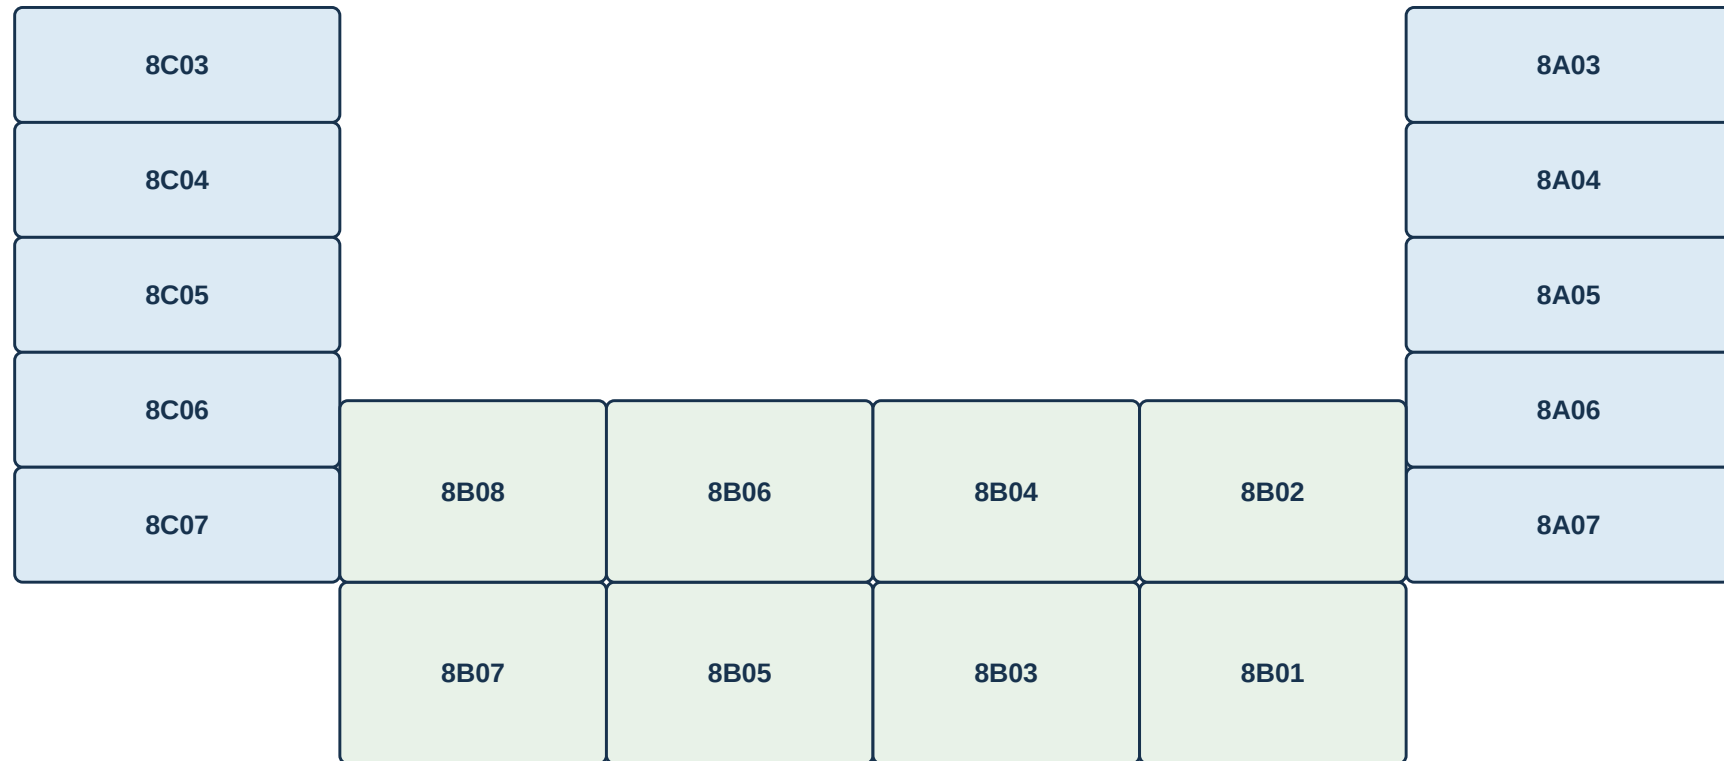

B-block: even rooms on top, odd rooms below

Central circulation / connecting block

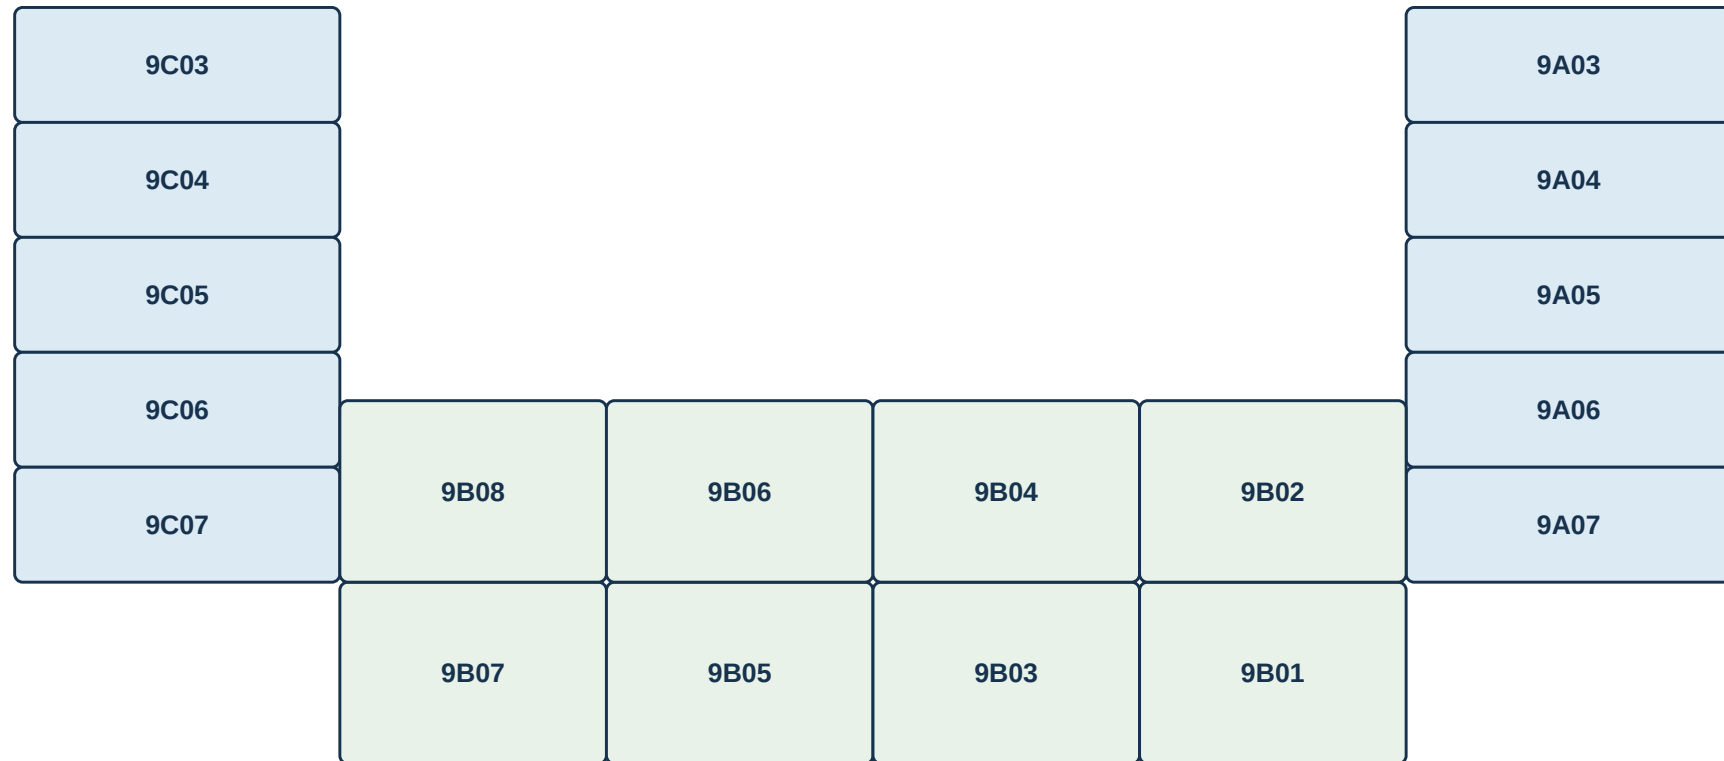

B-block: even rooms on top, odd rooms below

Central circulation / connecting block

Floor group	Classrooms	Other labeled spaces	Total usable spaces
Ground floor	0	4	4
1st floor	5	2	7
2nd-9th floors (8 floors)	144	0	144
TOTAL	149	6	155

Counting assumptions

- X spaces are excluded because they are inaccessible or non-existent.
- Classroom count includes A, B, and C labeled rooms.
- T.T. Ground, canteens, Girls Common Room, Study Room, and Library are counted as other labeled spaces.
- The upper-floor template is applied identically to floors 2 through 9.